


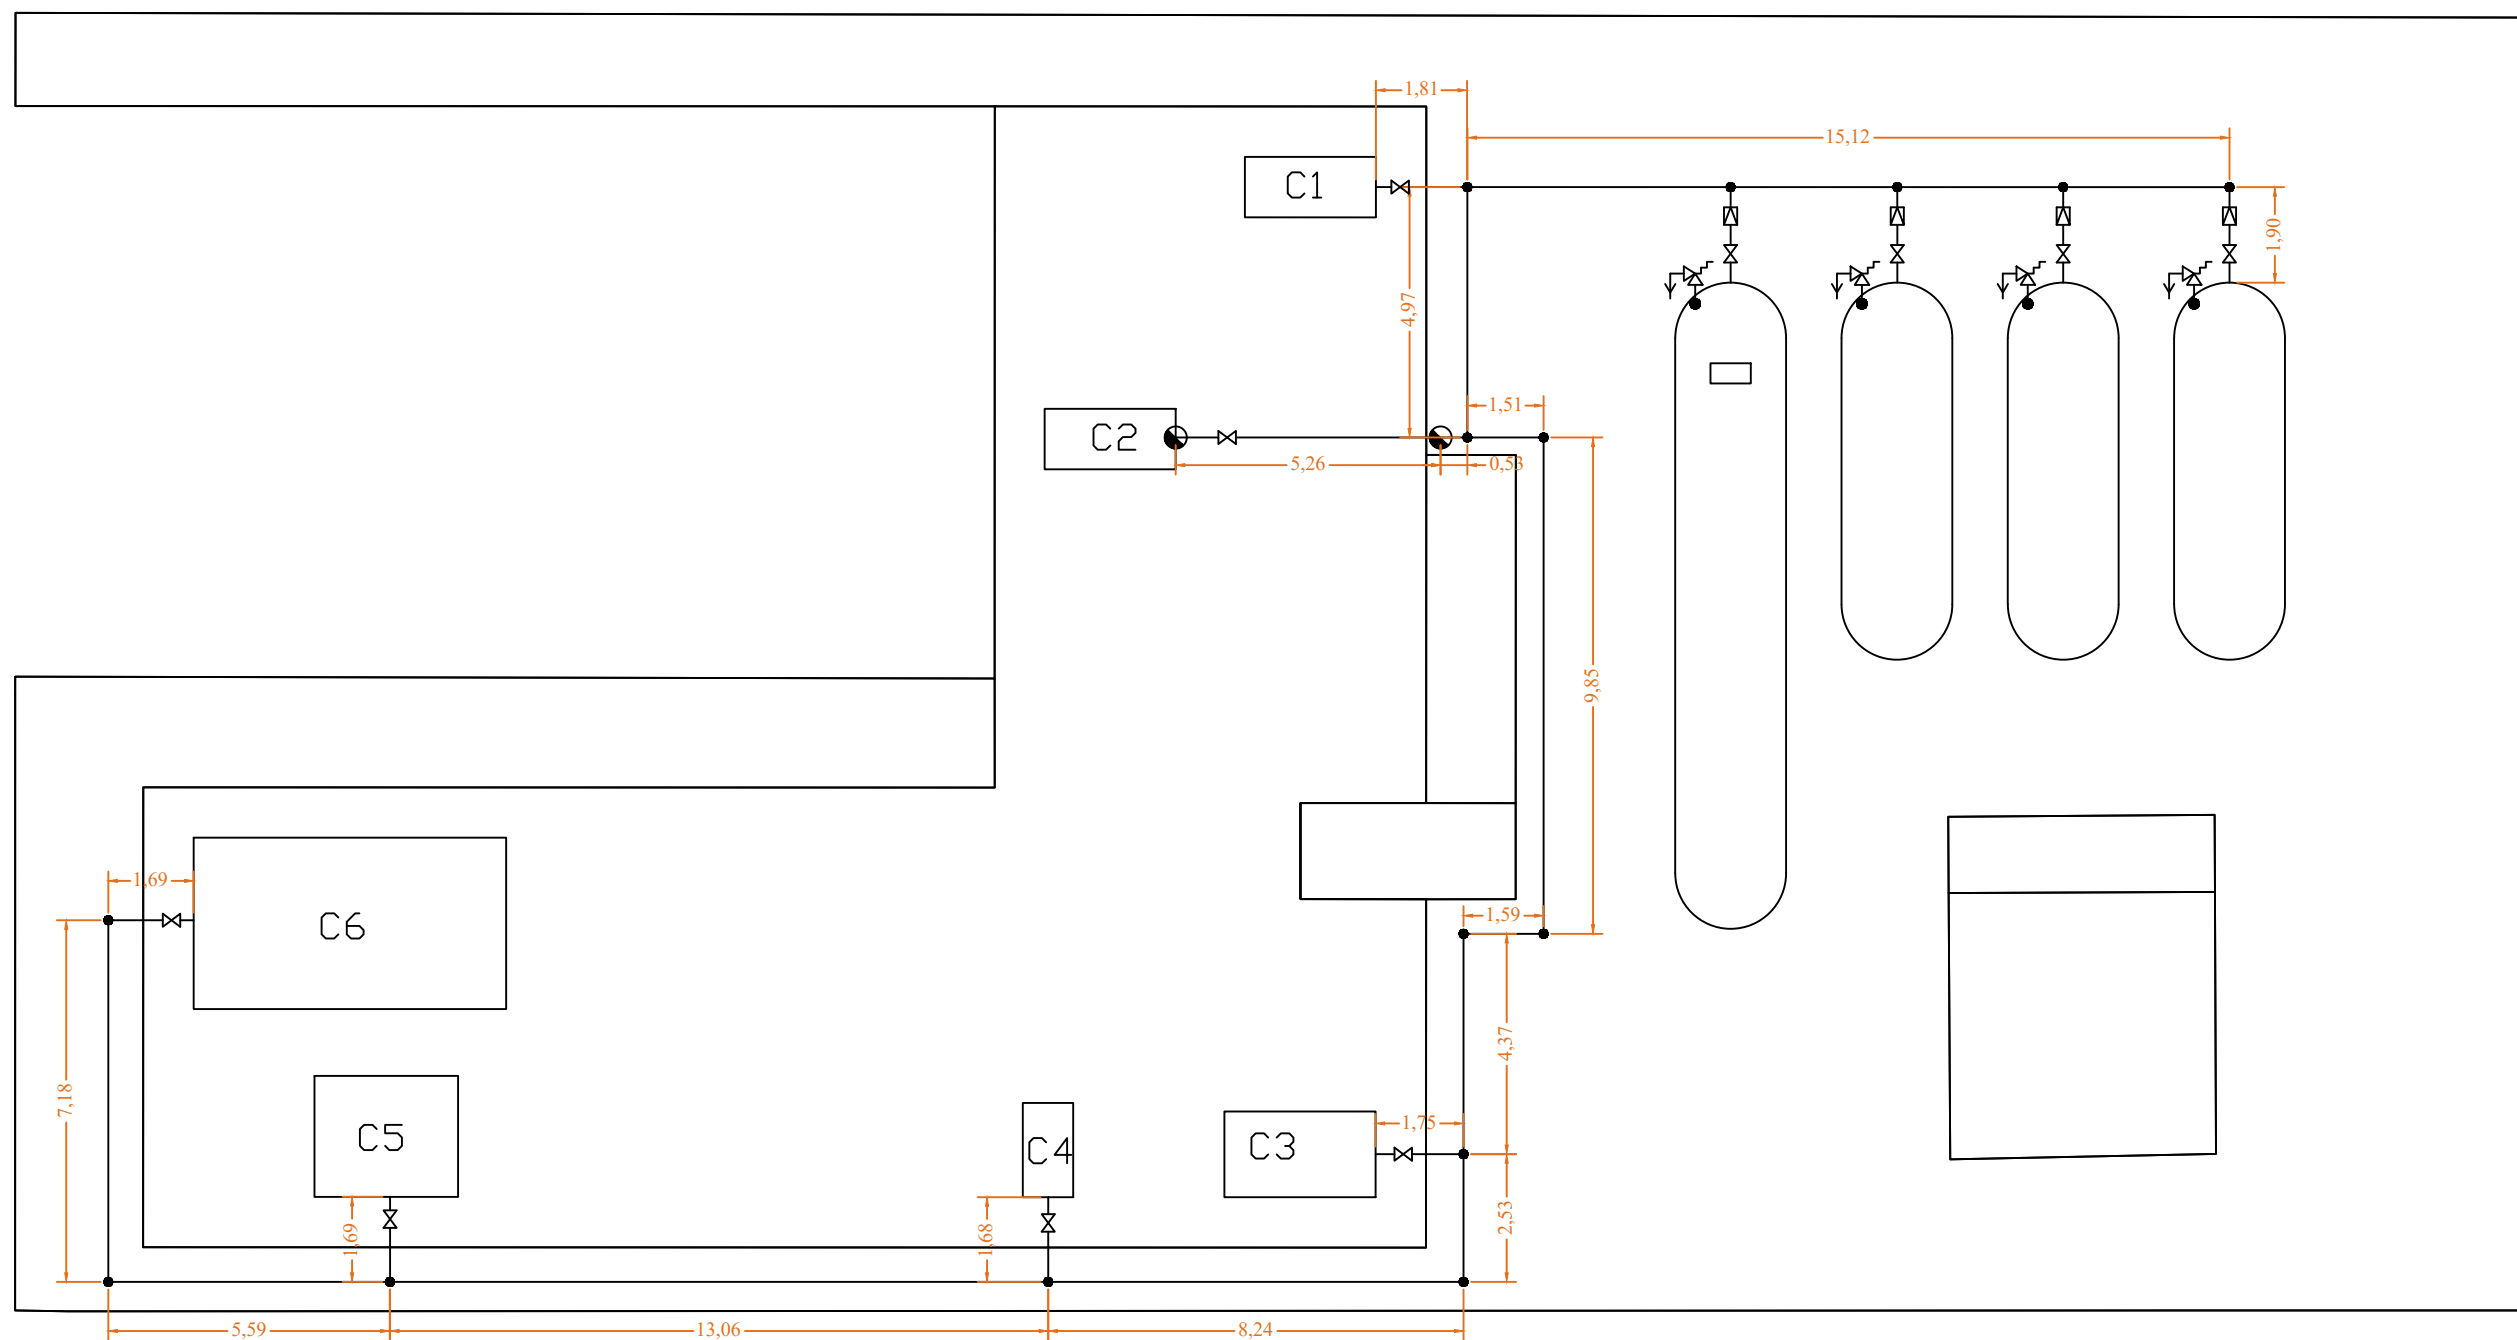

UNIVERSIDAD DE LEÓN ESCUELA DE INGENIERÍAS INDUSTRIAL, INFORMÁTICA Y AEROSPAIAL		PROYECTO: DISEÑO Y CÁLCULO DE UNA INSTALACIÓN DE GLP	
PLANO:	DIAGRAMA DE LA INSTALACIÓN	ESCALA: 1:150	FECHA: 05/2026
LOS ALUMNOS: Alberto España Carrete Carlos Fernández Palanca Rubén Modino López Juan Diego Niño González		PRÁCTICA INSTALACIONES II	Nº PLANO: 3