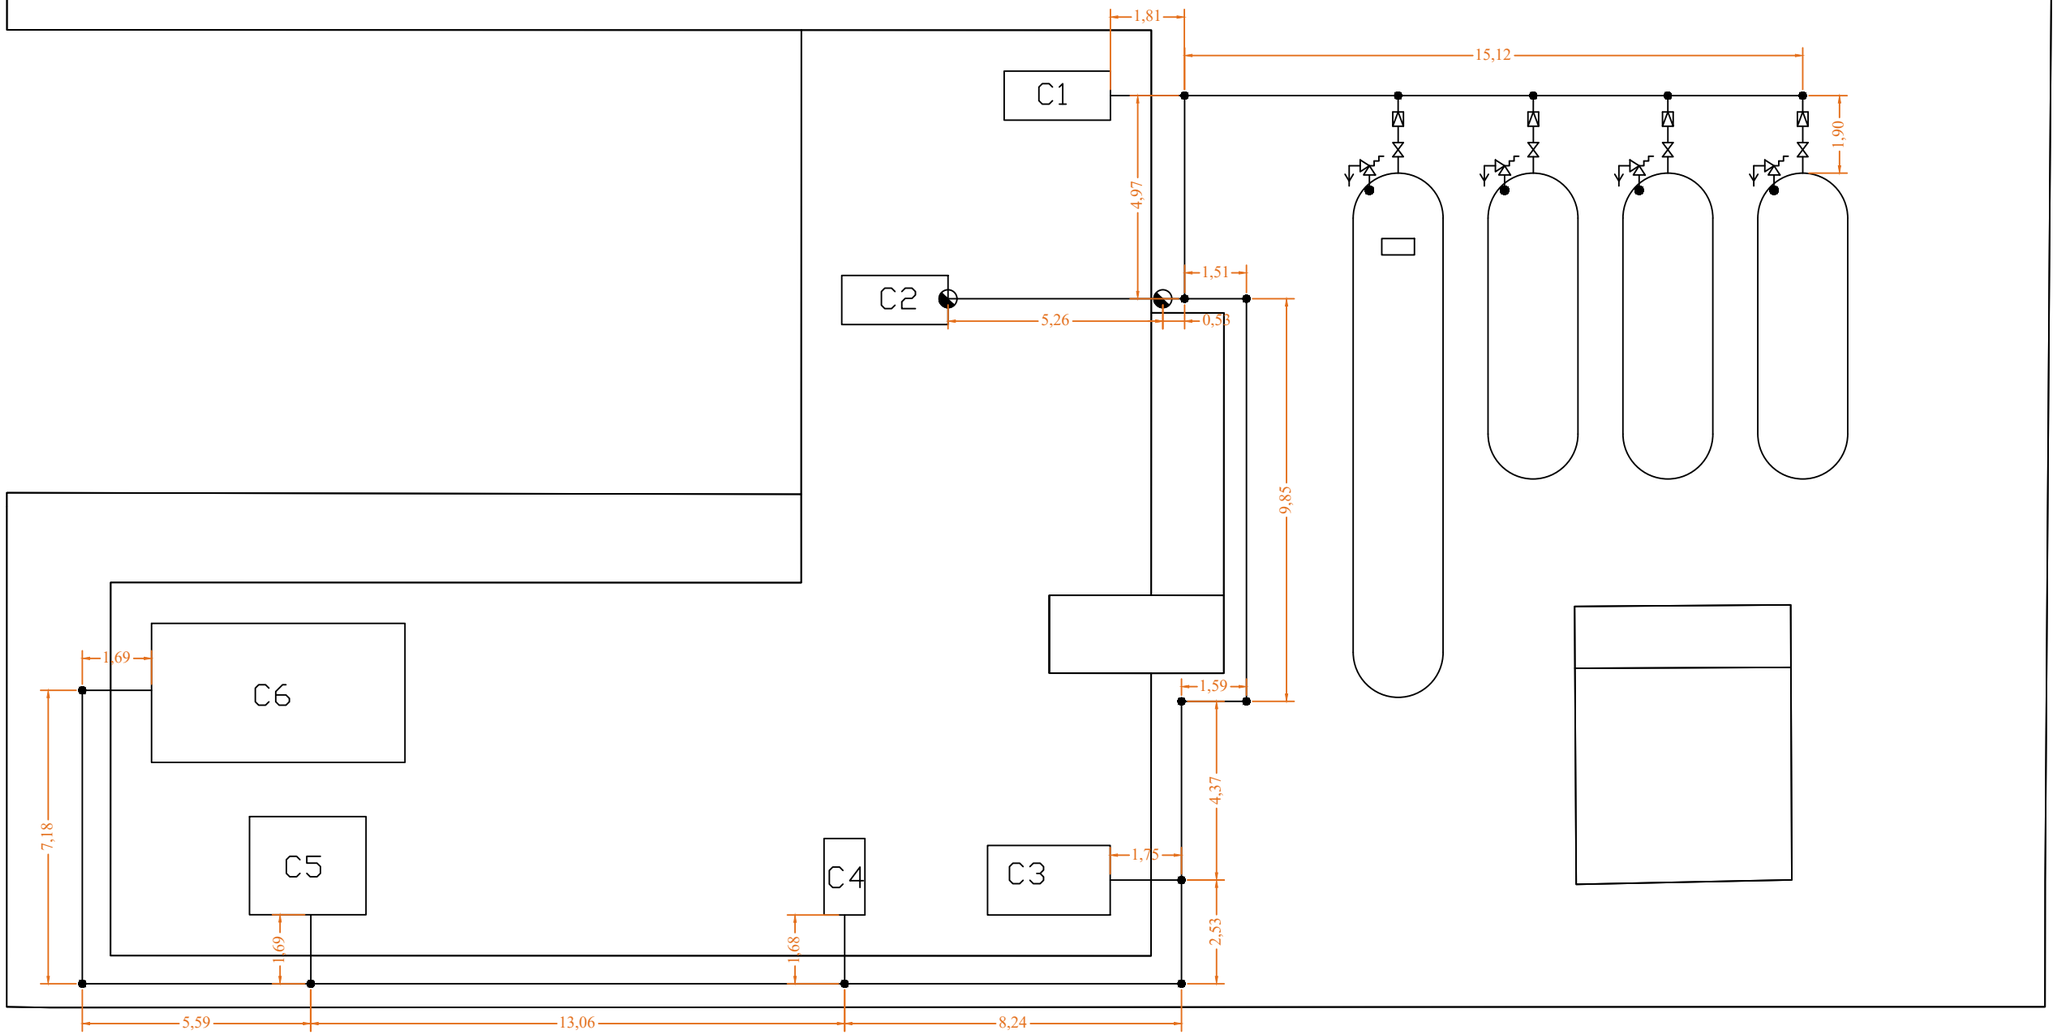



# UNIVERSIDAD DE LEÓN

**ESCUELA DE INGENIERÍAS INDUSTRIAL, INFORMÁTICA Y AEROESPACIAL**

***PROYECTO:***

DISEÑO Y CÁLCULO DE
UNA INSTALACIÓN DE GLP

***PLANO:***

DIAGRAMA DE LA INSTALACIÓN

***ESCALA:***

1:150

***FECHA:***

05/2026

***Nº PLANO:***

**3**

***LOS ALUMNOS:***

**Alberto España Carrete**
**Carlos Fernández Palanca**
**Rubén Modino López**
**Juan Diego Niño González**

PRÁCTICA INSTALACIONES II